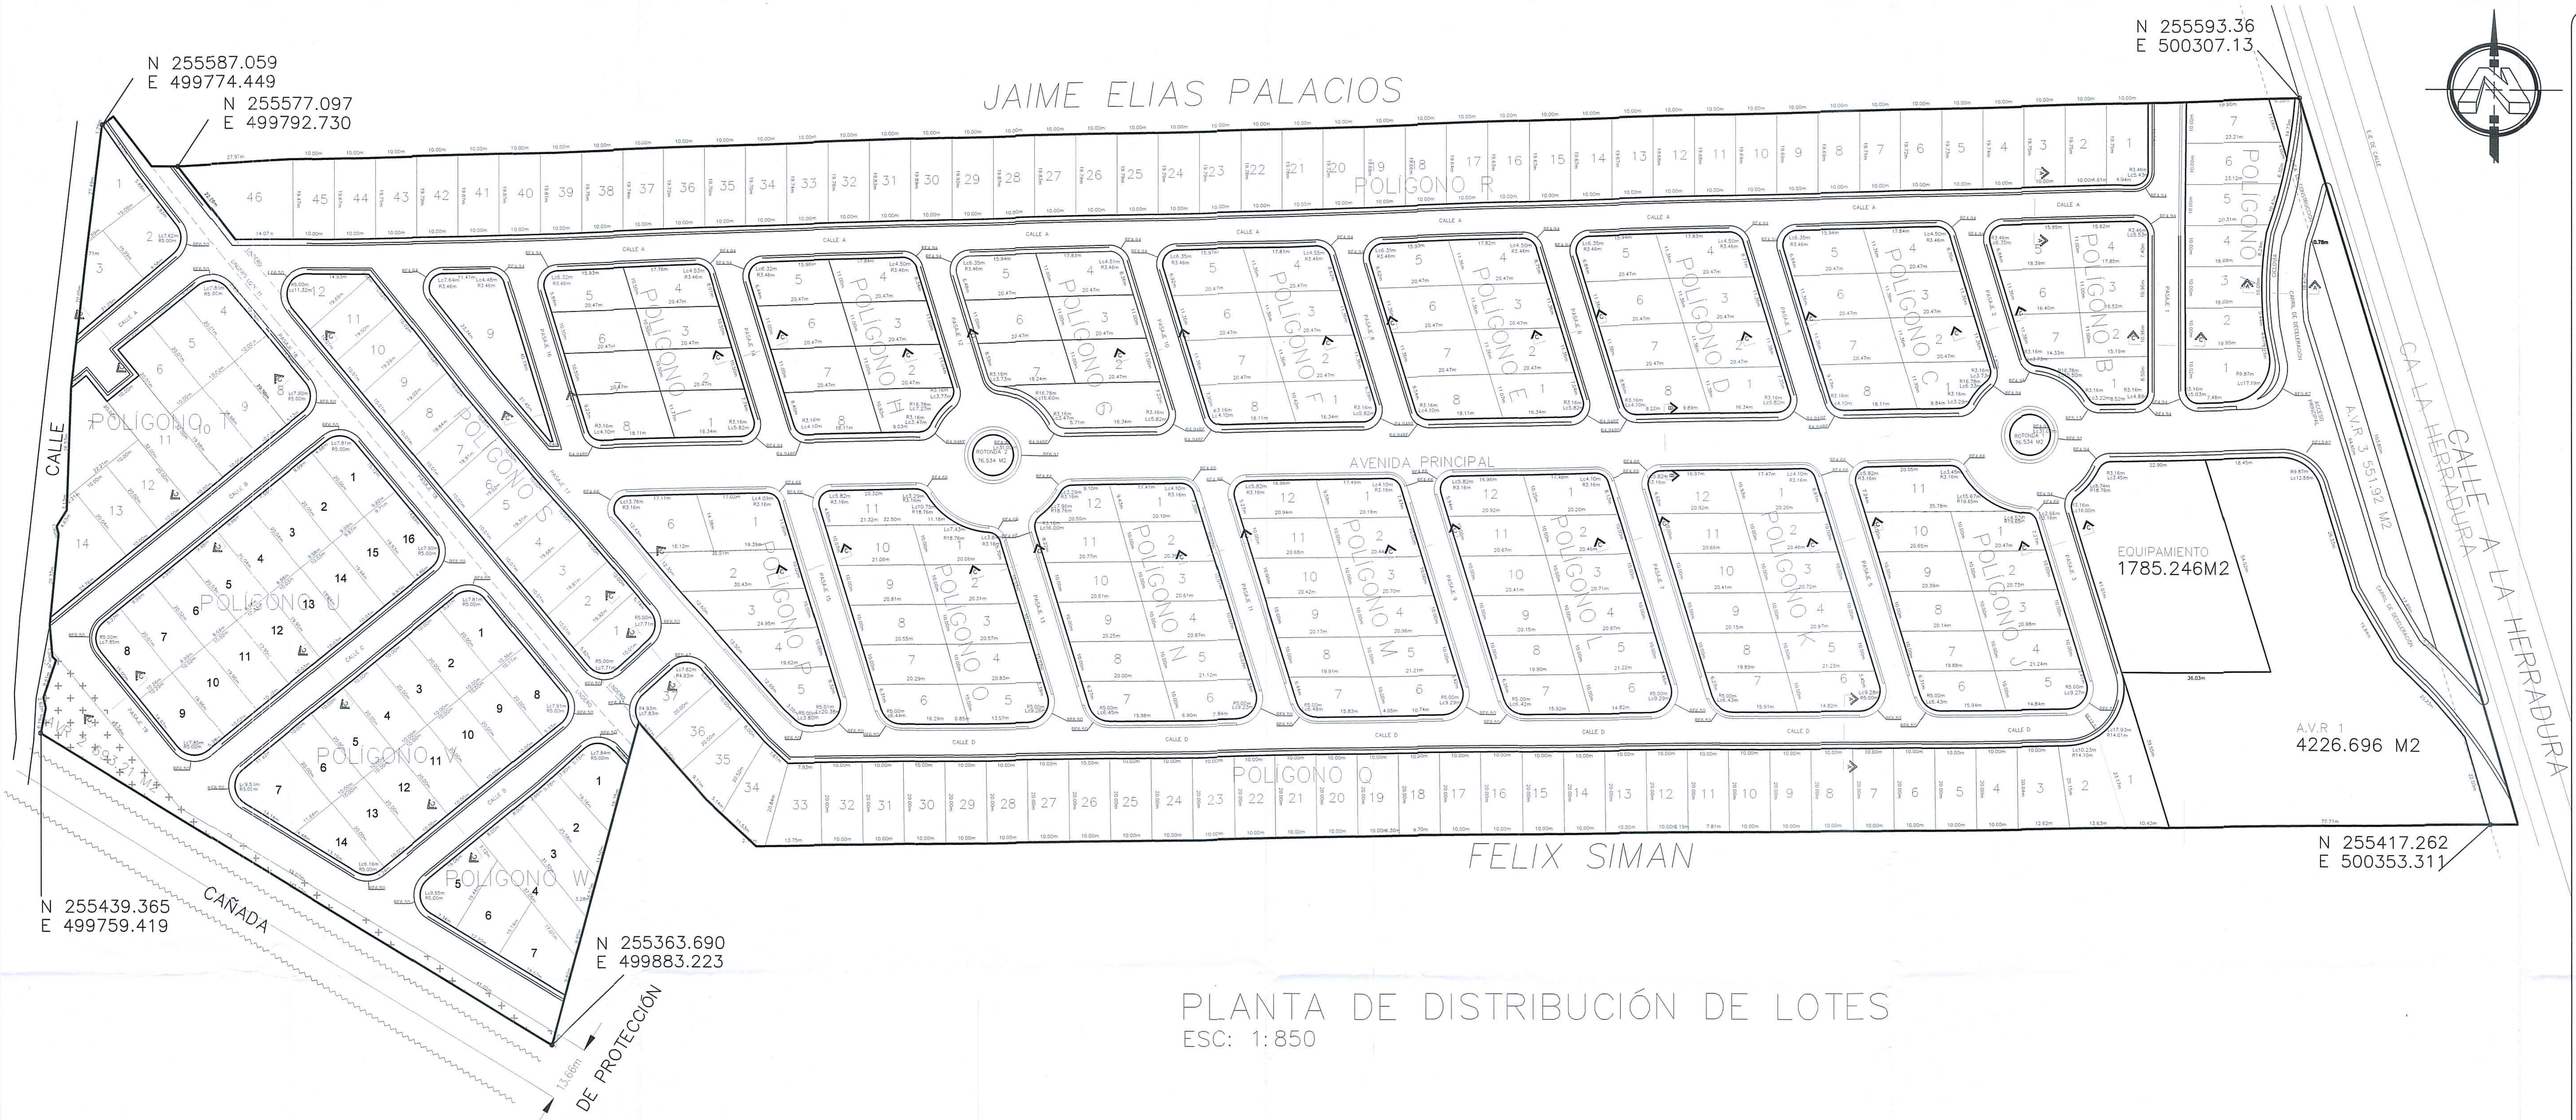

PLANTA DE DISTRIBUCIÓN DE LOTES

ESC: 1:850

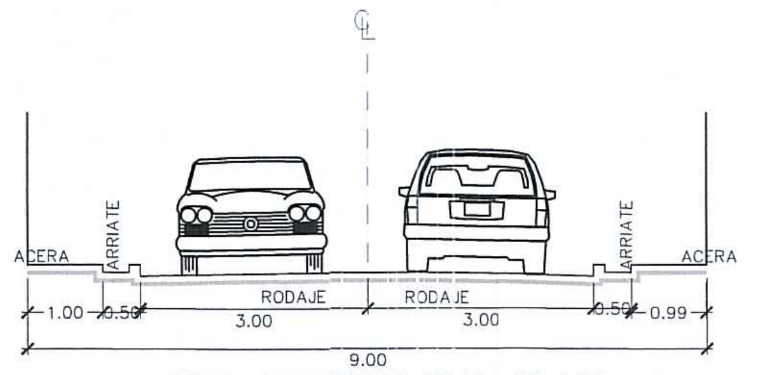

PERFIL DE DERECHO DE VIA DE 9.00 metros
SECCION C – C ESC 1:100

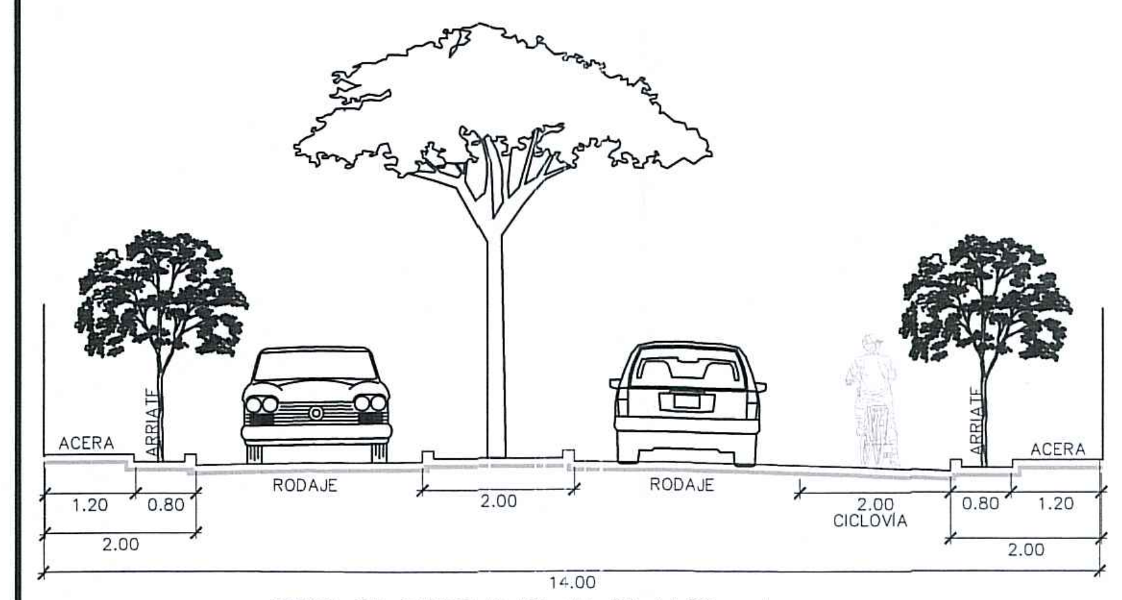

PERFIL DE DERECHO DE VIA DE 14.00 metros
SECCION B – B ESC 1:100

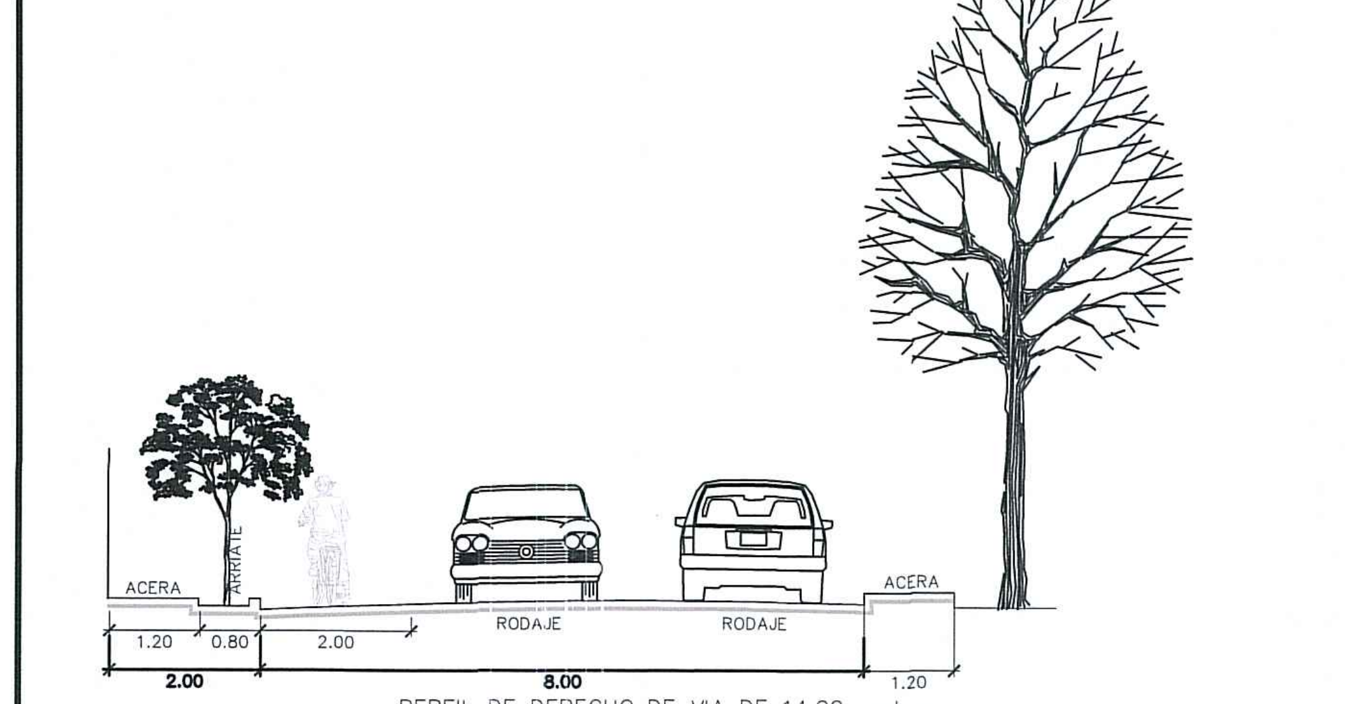

PERFIL DE DERECHO DE VIA DE 14.00 metros
SECCION A – A ESC 1:100

MANZANA	LOTE	AREA M2	PERIMETRO	AREA V2
A	1	242.61	60.95	347.13
	2	191.24	58.66	273.63
	3	185.36	57.28	265.22
	4	192.61	59.15	275.59
	5	217.84	63.84	311.69
	6	237.99	66.65	340.52
	7	222.22	64.17	317.96
ÁREA TOTAL		1489.87		2131.75

MANZANA	LOTE	AREA M2	PERIMETRO	AREA V2
C	1	193.02	57.17	276.18
	2	224.20	63.65	320.79
	3	224.20	63.65	320.79
	4	222.68	62.87	318.62
	5	219.71	60.96	314.37
	6	224.20	63.65	320.79
	7	224.20	63.65	320.79
	8	228.61	63.55	327.10
ÁREA TOTAL		1760.82		2519.43

MANZANA	LOTE	AREA M2	PERIMETRO	AREA V2
E	1	215.88	60.74	308.89
	2	224.20	63.65	320.79
	3	224.20	63.65	320.79
	4	223.55	62.90	319.86
	5	217.03	60.68	310.53
	6	224.20	63.65	320.79
	7	224.20	63.65	320.79
	8	216.17	62.29	309.30
ÁREA TOTAL		1769.43		2531.75

MANZANA	LOTE	AREA M2	PERIMETRO	AREA V2
G	1	331.35	93.70	474.10
	2	217.17	62.93	310.73
	3	217.17	62.93	310.73
	4	215.84	62.16	308.83
	5	212.51	60.23	304.07
	6	217.17	62.93	310.73
	7	216.06	62.23	309.14
ÁREA TOTAL		1627.27		2328.34

MANZANA	LOTE	AREA M2	PERIMETRO	AREA V2
I	1	229.79	62.14	328.79
	2	207.30	61.93	296.61
	3	207.30	61.93	296.61
	4	207.63	61.27	297.08
	5	201.03	59.06	287.64
	6	207.30	61.93	296.61
	7	207.30	61.93	296.61
	8	229.89	63.68	328.93
	9	445.15	108.92	636.93
ÁREA TOTAL		2142.69		3065.82

MANZANA	LOTE	AREA M2	PERIMETRO	AREA V2
K	1	212.87	61.52	304.58
	2	196.57	60.73	281.26
	3	199.05	61.25	284.81
	4	201.53	61.76	288.35
	5	204.01	62.27	291.90
	6	196.91	58.78	281.74
	7	187.91	58.50	268.87
	8	193.56	60.11	276.95
	9	196.04	60.62	280.50
	10	198.51	61.14	284.03
	11	200.99	61.65	287.58
	12	216.31	61.26	309.50
ÁREA TOTAL		2404.26		3440.08

MANZANA	LOTE	AREA M2	PERIMETRO	AREA V2
B	1	221.28	73.27	316.61
	2	173.69	53.67	248.52
	3	188.25	56.33	269.35
	4	200.06	68.40	286.25
	5	207.70	69.43	297.18
	6	190.52	57.14	272.60
	7	168.73	53.12	241.42
ÁREA TOTAL		1350.23		1931.95

MANZANA	LOTE	AREA M2	PERIMETRO	AREA V2
D	1	222.08	61.36	317.76
	2	224.75	63.70	321.58
	3	224.20	63.65	320.79
	4	222.79	62.87	318.77
	5	219.61	60.95	314.22
	6	224.20	63.65	320.79
	7	224.75	63.70	321.58
	8	222.36	62.92	318.16
ÁREA TOTAL		1784.74		2553.66

MANZANA	LOTE	AREA M2	PERIMETRO	AREA V2
F	1	203.13	59.44	290.64
	2	224.20	63.65	320.79
	3	224.20	63.65	320.79
	4	220.70	62.81	315.78
	5	221.08	61.06	316.33
	6	224.20	63.65	320.79
	7	224.20	63.65	320.79
	8	203.41	61.00	291.04
ÁREA TOTAL		1745.12		2496.97

MANZANA	LOTE	AREA M2	PERIMETRO	AREA V2
H	1	168.97	54.93	241.77
	2	217.17	62.97	310.73
	3	217.17	62.93	310.73
	4	215.63	62.15	308.53
	5	212.35	60.19	303.84
	6	217.17	62.93	310.73
	7	217.17	62.93	310.73
	8	213.36	62.00	305.28
ÁREA TOTAL		1678.99		2402.35

MANZANA	LOTE	AREA M2	PERIMETRO	AREA V2
J	1	193.38	59.80	276.69
	2	199.16	61.27	284.96
	3	201.64	61.78	288.51
	4	204.12	62.29	292.06
	5	196.46	68.75	281.10
	6	188.29	68.51	269.41
	7	193.45	60.09	276.79
	8	195.93	60.60	280.34
	9	198.41	61.11	283.89
	10	200.89	61.63	287.44
	11	317.84	88.02	454.77
ÁREA TOTAL		2289.57		3275.98

MANZANA	LOTE	AREA M2	PERIMETRO	AREA V2
L	1	199.71	77.64	285.75
	2	196.52	60.72	281.19
	3	199.00	61.24	284.73
	4	201.48	61.75	288.28
	5	203.96	62.26	291.83
	6	197.05	58.79	281.94
	7	187.79	58.50	268.70
	8	193.61	60.12	277.02
	9	196.09	60.63	280.57
	10	198.57	61.15	284.12
	11	201.05	61.66	287.67
	12	202.44	76.85	289.66
ÁREA TOTAL		2377.27		3401.46

MANZANA	LOTE	AREA M2	PERIMETRO	AREA V2
M	1	186.92	58.83	267.45
	2	196.40	60.70	281.01
	3	198.88	61.21	284.56
	4	201.35	61.72	288.10
	5	203.83	62.24	291.65
	6	196.05	58.71	280.51
	7	190.00	58.66	271.86
	8	193.73	60.15	277.19
	9	196.21	60.66	280.74
	10	198.69	61.17	284.29
	11	201.17	61.68	287.84
	12	189.11	58.58	270.58
ÁREA TOTAL		2352.34		3365.79

MANZANA	LOTE	AREA M2	PERIMETRO	AREA V2
N	1	182.95	58.33	261.77
	2	195.56	60.52	279.81
	3	198.04	61.04	283.36
	4	200.52	61.55	286.91
	5	202.99	62.06	290.44
	6	194.55	58.43	278.37
	7	189.66	58.76	271.37
	8	194.57	60.32	278.40
	9	197.05	60.83	281.94
	10	199.53	61.35	285.49
	11	201.70	61.29	288.60
	12	139.10	52.16	199.03
ÁREA TOTAL		2296.22		3285.50

MANZANA	LOTE	AREA M2	PERIMETRO	AREA V2
O	1	179.53	58.12	256.88
	2	195.16	60.44	279.24
	3	197.64	60.95	282.79
	4	200.12	61.86	286.34
	5	192.24	57.90	275.06
	6	192.21	59.33	275.02
	7	197.45	60.91	282.52
	8	199.93	61.43	286.07
	9	202.41	61.94	289.61
	10	204.88	62.45	293.15
	11	240.93	77.27	344.73
ÁREA TOTAL		2202.50		3151.40

MANZANA	LOTE	AREA M2	PERIMETRO	AREA V2
P	1	267.02	66.78	382.06
	2	318.04	88.29	455.06
	3	267.17	77.99	382.27
	4	214.59	67.06	307.04
	5	209.63	60.01	299.94
	6	267.69	66.20	383.02
ÁREA TOTAL		1544.14		2209.40

MANZANA	LOTE	AREA M2	PERIMETRO	AREA V2
S	1	208.836	57.60	298.81
	2	198.62	59.74	284.19
	3	197.55	59.51	282.66
	4	195.21	59.00	279.31
	5	191.25	58.34	273.65
	6	189.65	57.94	271.36
	7	188.70	57.76	270.00
	8	188.91	57.88	270.30
	9	191.55	58.34	274.08
	10	194.06	58.82	277.67
	11	195.96	59.22	280.39
	12	154.62	53.54	221.23
ÁREA TOTAL		2294.92		3283.63

MANZANA	LOTE	AREA M2	PERIMETRO	AREA V2
T	1	200.00	68.86	286.17
	2	214.80	57.37	307.34
	3	200.00	63.89	286.17
	4	193.32	57.78	276.61
	5	200.12	60.02	286.34
	6	200.04	60.01	286.22
	7	269.44	73.48	385.52
	8	196.15	57.97	280.66
	9	199.85	59.97	285.95
	10	199.81	59.97	285.89
	11	320.00	84.00	457.86
	12	200.09	60.02	286.29
	13	200.28	60.06	286.57
	14	273.26	76.04	390.99
ÁREA TOTAL		3067.16		4388.58

MANZANA	LOTE	AREA M2	PERIMETRO	AREA V2
U	1	190.00	57.49	271.86
	2	200.42	60.10	286.77
	3	200.00	60.00	286.17
	4	200.00	60.00	286.17
	5	200.00	60.00	286.17
	6	200.00	60.02	286.17
	7	200.00	60.01	286.17
	8	200.00	58.39	286.17
	9	200.00	58.35	286.17
	10	200.00	59.96	286.17
	11	200.00	59.95	286.17
	12	200.00	59.95	286.17
	13	200.00	59.95	286.17
	14	200.00	59.94	286.17
	15	196.74	59.61	281.50
	16	190.00	57.29	271.86
ÁREA TOTAL		3177.16		4545.97

MANZANA	LOTE	AREA M2	PERIMETRO	AREA V2
V	1	200.00	58.43	286.17
	2	200.00	60.00	286.17
	3	200.00	60.00	286.17
	4	200.00	60.00	286.17
	5	200.00	60.00	286.17
	6	200.00	60.00	286.17
	7	291.78	66.95	417.49
	8	200.00	58.35	286.17
	9	200.00	60.00	286.17
	10	200.00	60.00	286.17
	11	200.00	60.00	286.17
	12	200.00	60.00	286.17
	13	200.00	60.00	286.17
	14	163.84	56.90	234.43
ÁREA TOTAL		2855.62		4085.90

MANZANA	LOTE	AREA M2	PERIMETRO	AREA V2
W	1	200.00	57.89	286.17
	2	200.00	60.00	286.17
	3	227.59	74.75	325.64
	4	273.53	86.23	391.37
	5	210.87	59.51	301.72
	6	210.87	59.71	301.72
	7	210.89	60.89	301.75
ÁREA TOTAL		1533.75		2194.53

MANZANA	LOTE	AREA M2	PERIMETRO	AREA V2
Q	1	281.90	91.08	403.35
	2	245.87	67.02	351.80
	3	226.19	62.81	323.64
	4	200.00	60.04	286.17
	5	200.00	60.00	286.17
	6	200.00	60.00	286.17
	7	200.00	60.00	286.17
	8	200.00	60.00	286.17
	9	200.00	60.00	286.17
	10	200.00	60.00	286.17
	11	200.00	60.00	286.17
	12	200.00	60.00	286.17
	13	200.00	60.00	286.17
	14	200.00	60.00	286.17
	15	200.00	60.00	286.17
	16	200.00	60.00	286.17
	17	200.00	60.00	286.17
	18	200.00	60.00	286.17
	19	200.01	60.00	286.18
	20	200.01	60.00	286.18
	21	200.01	60.00	286.18
	22	200.01	60.00	286.18
	23	200.01	60.00	286.18
	24	200.00	60.00	286.17
	25	200.00	60.00	286.17
	26	200.00	60.00	286.17
	27	200.00	60.00	286.17
	28	200.00	60.00	286.17
	29	200.00	60.00	286.17
	30	200.00	60.00	286.17
	31	200.00	60.00	286.17
	32	200.00	60.00	286.17
	33	216.80	62.52	310.20
	34	216.00	62.97	309.06
	35	222.64	62.77	318.56
	36	200.00	60.00	286.17
	37	189.29	55.73	270.84
ÁREA TOTAL		7598.74		10872.49

CUADRO DE ÁREAS VERDES		
NOMBRE	ÁREA M2	ÁREA V2
ROTONDA 1	76.53	109.50
ROTONDA 2	76.53	109.50
A.V.R. 3	551.92	789.70
A.V.R. 2	693.21	991.86
A.V.R. 1	4226.67	6047.64
ÁREA VERDE TOTAL	5624.86	8048.21

MANZANA	LOTE	AREA M2	PERIMETRO	AREA V2
R	1	195.97	58.27	280.40
	2	197.42	59.50	282.47
	3	197.41	59.50	282.46
	4	197.35	59.49	282.37
	5	197.23	59.46	282.20
	6	197.12	59.44	282.04
	7	197.02	59.42	281.90
	8	196.92	59.40	281.76
	9	196.83	59.38	281.63
	10	196.79	59.37	281.57
	11	196.75	59.37	281.52
	12	196.71	59.36	281.46
	13	196.67	59.35	281.40
	14	196.63	59.34	281.34
	15	196.59	59.33	281.29
	16	196.49	59.30	281.14
	17	196.25	59.28	280.80
	18	196.41	59.30	281.03
	19	196.57	59.34	281.26
	20	196.94	59.41	281.79
	21	197.42	59.51	282.47
	22	197.75	59.56	282.95
	23	197.77	59.57	282.97
	24	197.79	59.57	283.00
	25	197.80	59.58	283.02
	26	197.82	59.58	283.05
	27	197.95	59.62	283.23
	28	198.41	59.70	283.89
	29	198.89	59.79	284.58
	30	199.12	59.82	284.91
	31	198.51	59.72	284.03
	32	197.93	59.61	283.20
	33	197.53	59.53	282.63
	34	197.14	59.45	282.07
	35	196.90	59.41	281.73
	36	197.04	59.43	281.93
	37	197.20	59.46	282.16
	38	197.37	59.50	282.40
	39	197.67	59.56	282.83
	40	198.29	59.68	283.72
	41	198.81	59.74	284.46
	42	198.25	59.66	283.66
	43	197.42	59.50	282.47
	44	196.80	59.38	281.59
	45	195.73	59.14	280.06
	46	398.63	122.24	570.37
ÁREA TOTAL		9278.01		13275.24

CUADRO GENERAL DE ÁREAS		
DESCRIPCIÓN	AREA M2	AREA V2
AREA VERDE RECREATIVA	5,471.80	7829.20
AREA VERDE ECOLOGICA	153.06	219.00
EQUIPAMIENTO	1785.25	2554.39
CIRCULACIÓN	30,283.98	43331.17
LOTES (292)	59,087.07	84543.43
TOTAL	96,781.16	138477.20

CUADRO DE POLÍGONOS			
POLÍGONO	N°LOTES	ÁREA M2	ÁREA V2
A	7	1489.87	2131.75
B	7	1350.23	1931.95
C	8	1760.82	2519.43
D	8	1784.74	2553.66
E	8	1769.43	2531.75
F	8	1745.12	2496.97
G	7	1627.27	2328.34
H	8	1678.99	2402.35
I	9	2142.69	3065.82
J	11	2289.57	3275.98
K	12	2404.26	3440.08
L	12	2377.27	3401.46
M	12	2352.34	3365.79
N	12	2296.22	3285.50
O	11	2202.50	3151.40
P	6	1544.14	2209.40
Q	37	7598.74	10872.49
R	46	9278.01	13275.24
S	12	2294.92	3283.63
T	14	3067.16	4388.58
U	16	3177.16	4545.97
V	14	2855.62	4085.90
W	7	1533.75	2194.53
TOTAL	292	59087.07	84543.43

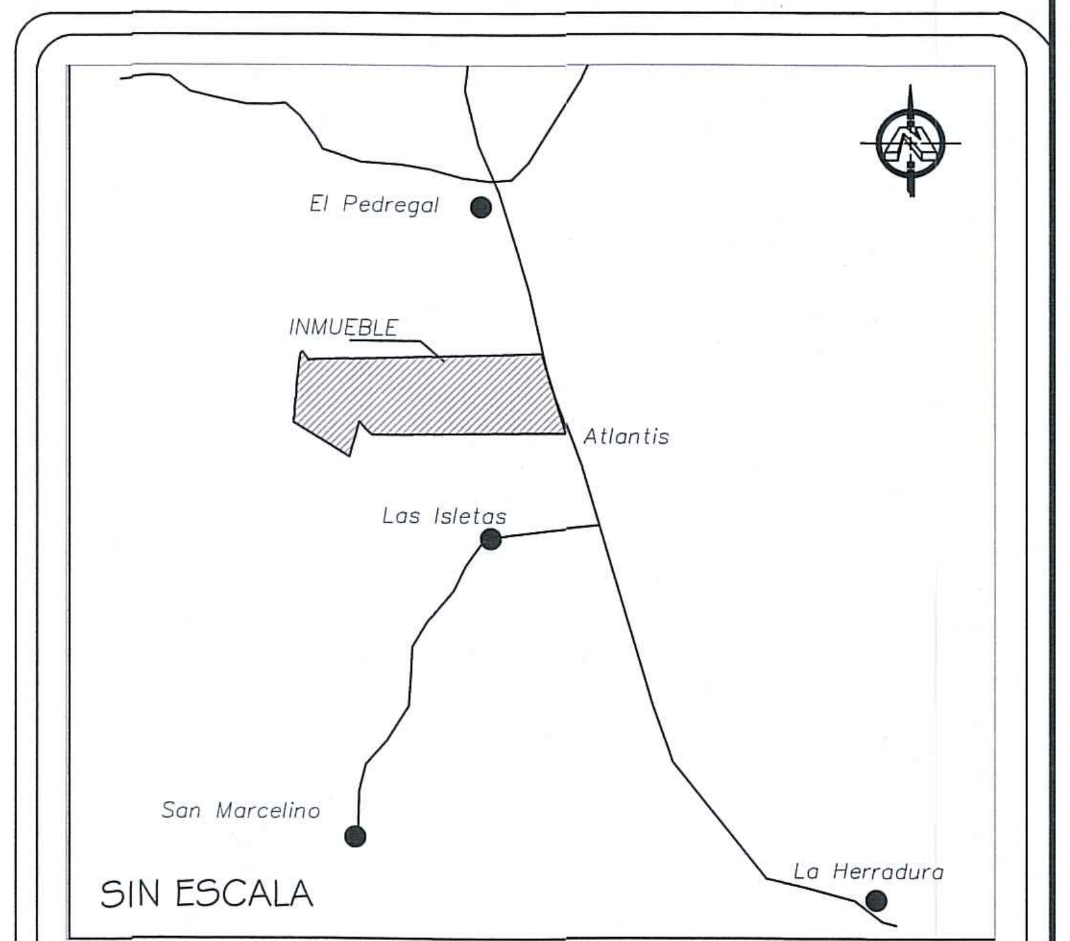

SIN ESCALA

ESQUEMA DE UBICACIÓN

PROYECTO:
PARCELACIÓN "PORTALES DE BELÉN"

CONTENIDO:
DISTRIBUCIÓN DE LOTES

PROPIETARIO:
INVERSIONES SANTA JULIA S.A DE C.V

MATRICULA:
55001959, 55001960, 55001961, 55001962–00000

DIRECCIÓN:
DCANTÓN LAS ISLETAS, CASERILLO LOS NOVILLOS, POL. I, LOTES 8, 9, 10 Y 11, SAN PEDRO MASAHUAT. DPTO. DE LA PAZ

MAPA CATASTRAL / PARCELA:
0815R11–15 / 0815R11–13 / 0815R11–33

ÁREA TOTAL:
96,781.16 M2

DIBUJO:

ENCARGADO DEL PROYECTO:

PRESENTA:

REGISTRO NACIONAL DE ARQUITECTOS E INGENIEROS
RAÚL ERNESTO OCHOA MOLINA
IC-7818
INGENIERO CIVIL

ARCHIVO:

FECHA:
FEBRERO 2025

ESCALA:
INDICADA

HOJA:
A 1/1

CUADRO DE SELLOS:

UPGOT
Unidad de Planificación Gestión y Ordenamiento Territorial
Alcaldía de La Paz Oeste
UNIDAD DE PLANIFICACIÓN GESTIÓN Y ORDENAMIENTO TERRITORIAL, ALCALDÍA MUNICIPAL DE LA PAZ OESTE, LA PAZ.
DICTAMEN TÉCNICO FAVORABLE
PROYECTO DE PARCELACIÓN
EXP. No. 34-25 FECHA: 10-02-2025
TÉCNICO-UPGOT LA PAZ OESTE
COORDINADOR-UPGOT LA PAZ OESTE

REFORMA

ALCALDÍA MUNICIPAL DE LA PAZ OESTE
PERMISO DE PROYECTO
PARCELACIÓN
EXP. No. 017-25 FECHA: 10-02-2025
ALCALDE MUNICIPAL